

PROJEKT MIESZKANIA

①

PROFIL INWESTORA


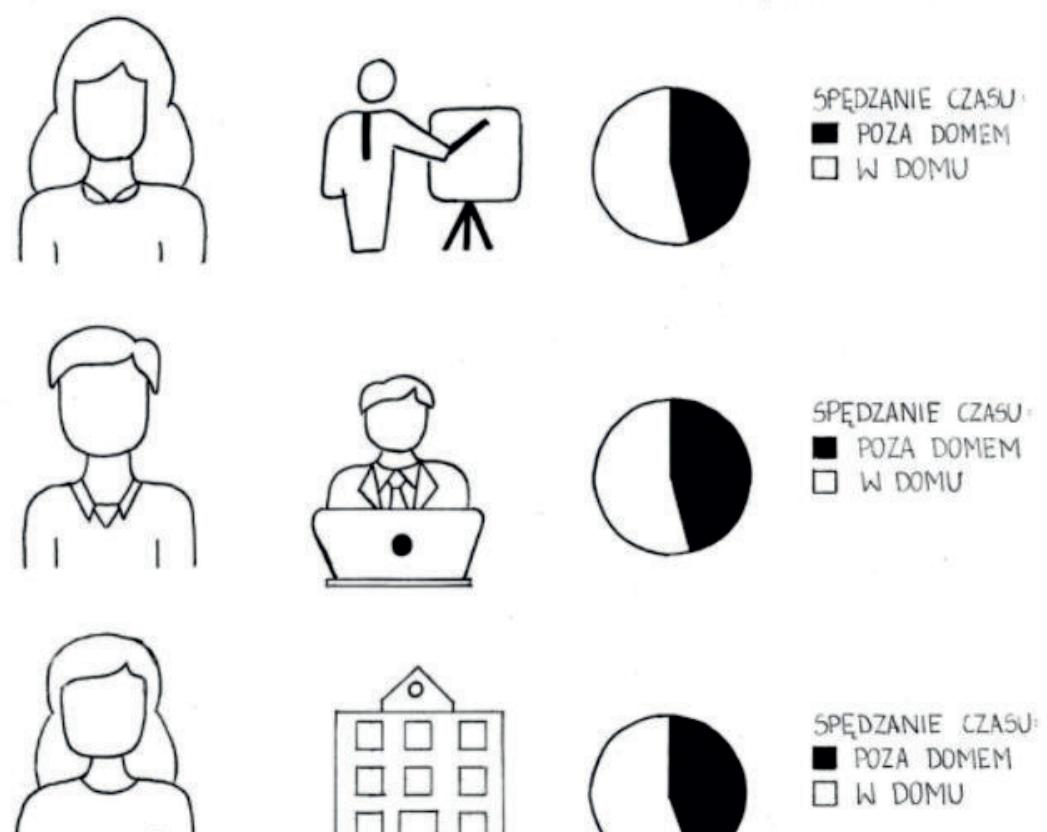


DIAGRAM POŁĄCZEŃ FUNKCJONALNYCH

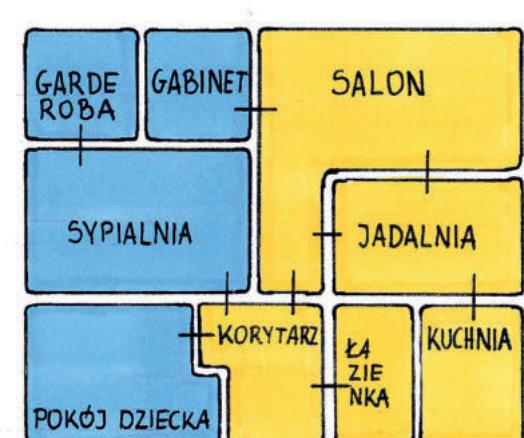


ANALIZA NASŁONECZNENIA

RÓWNO NOC WIOSENNA I JESIENNA
W GODZINACH 7:00 - 17:00

CZAS NASŁONECZNENIA:


OK. 6H
7H 15 MIN
7H 45 MIN

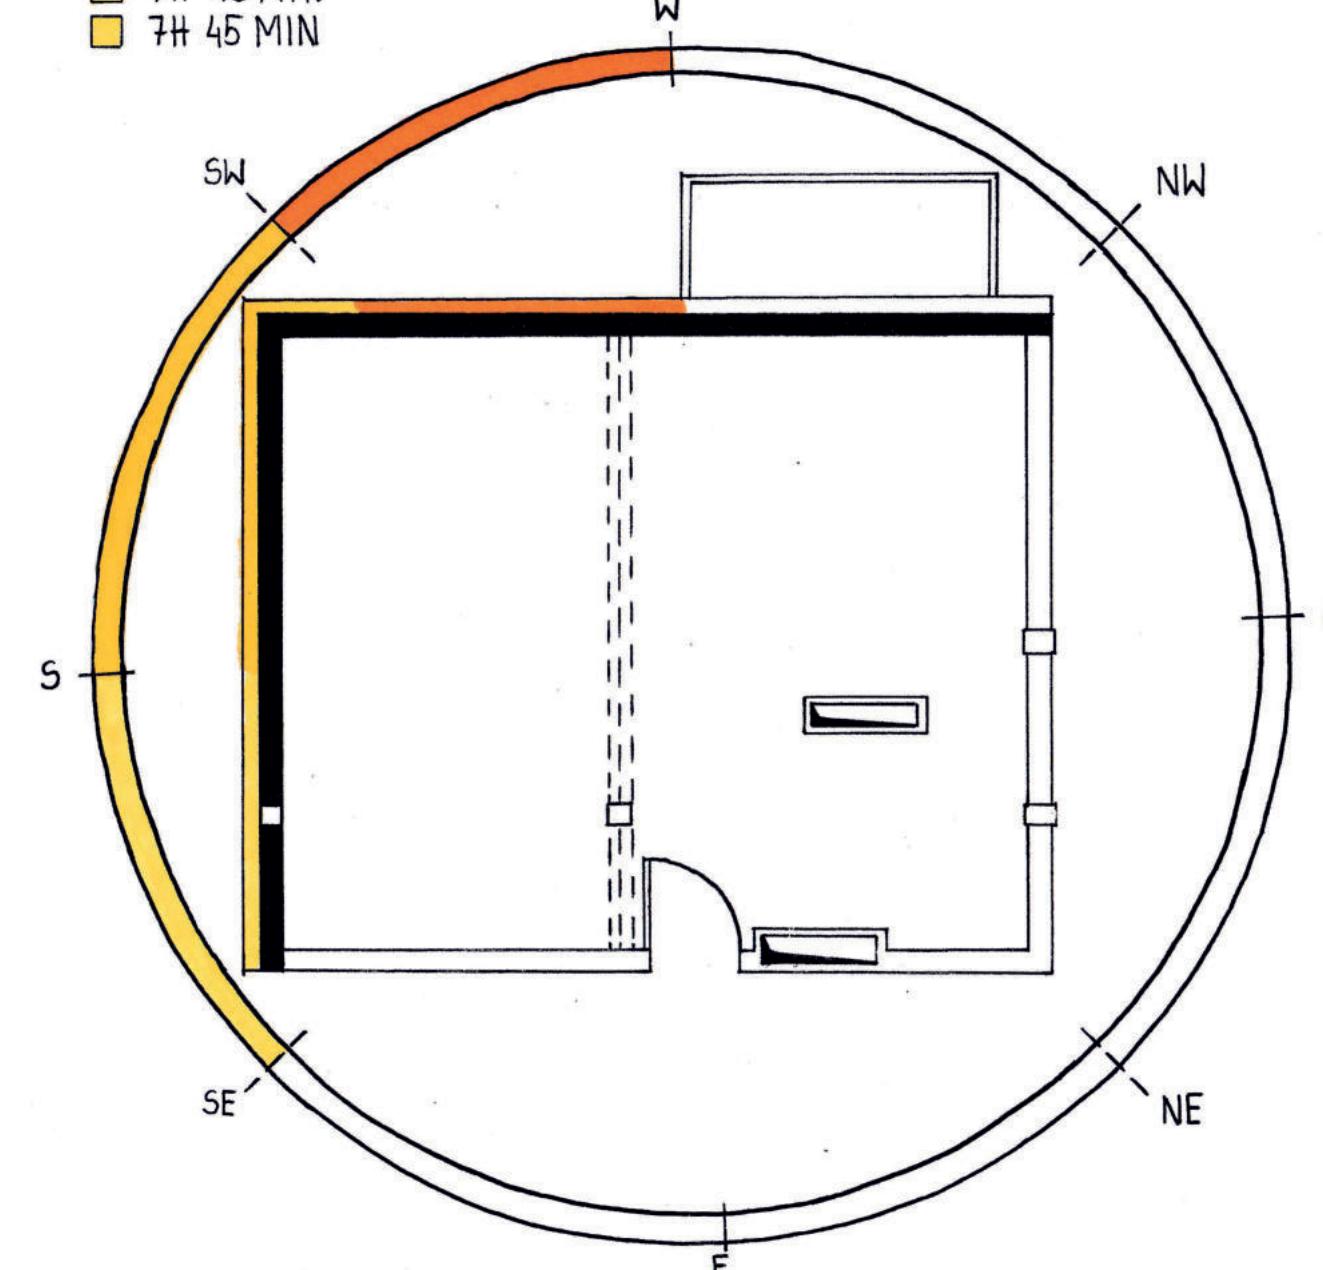


ANALIZA STREF

STREFA DZIENNA

ANALIZA OPARTA NA § 60
WARUNKÓW TECHNICZNYCH

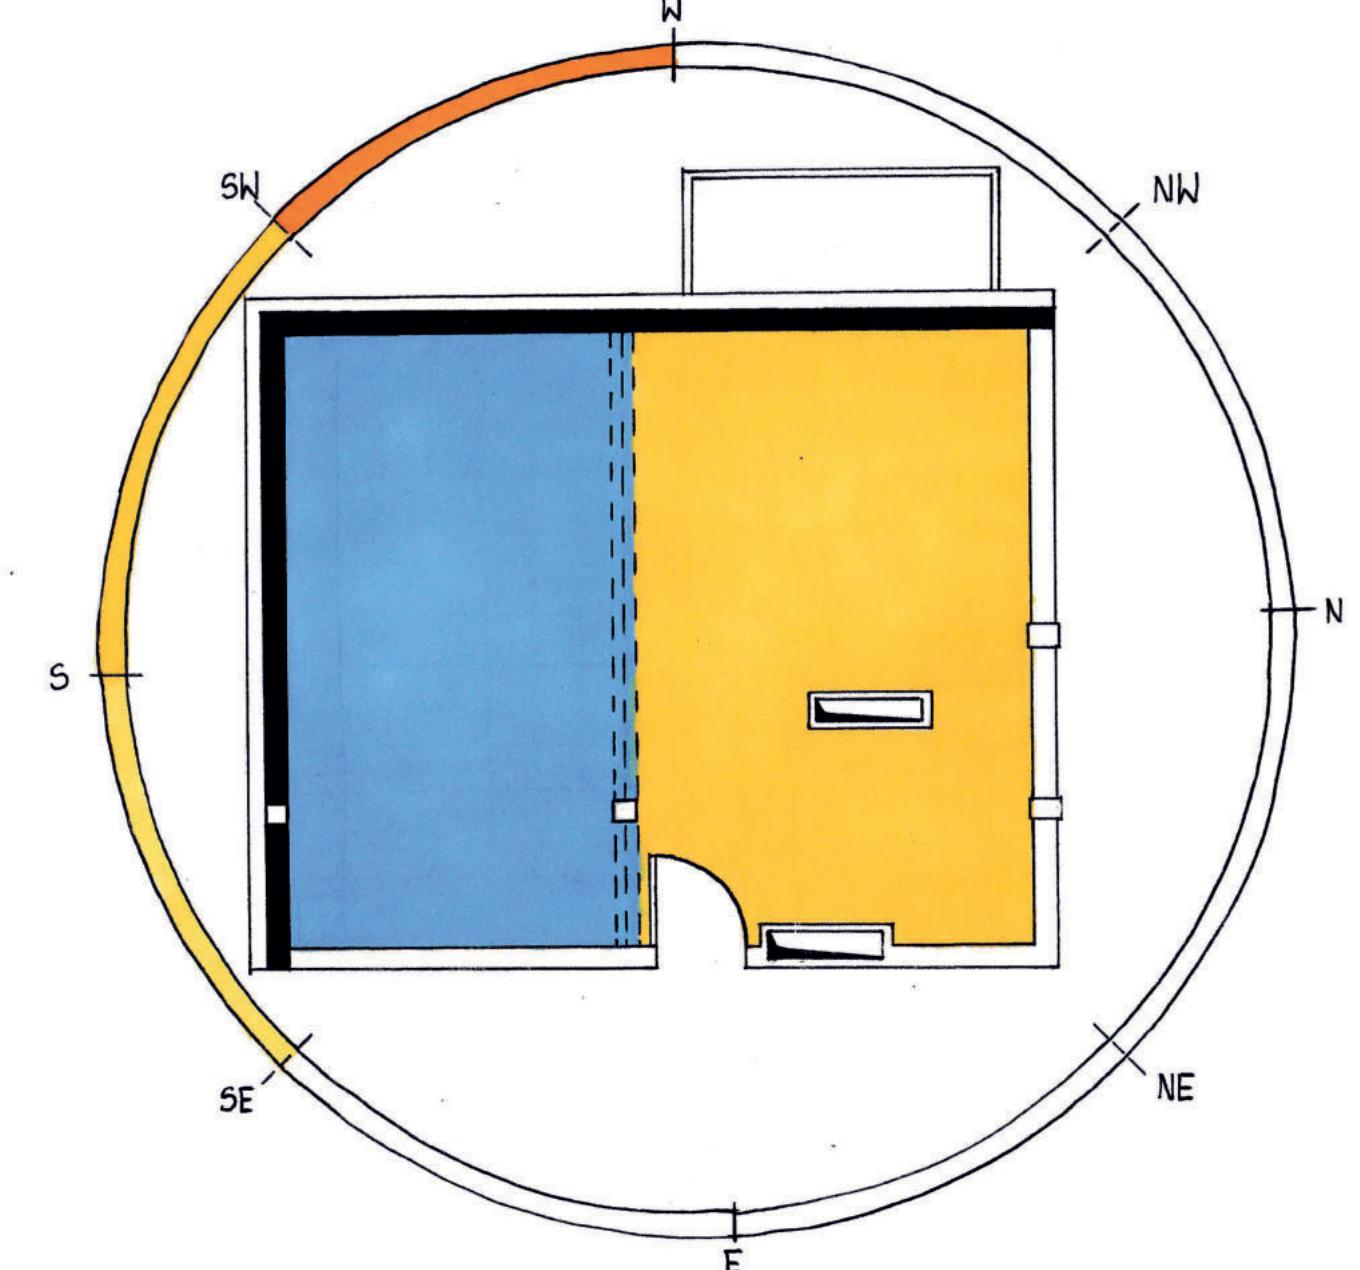

RZUT MIESZKANIA

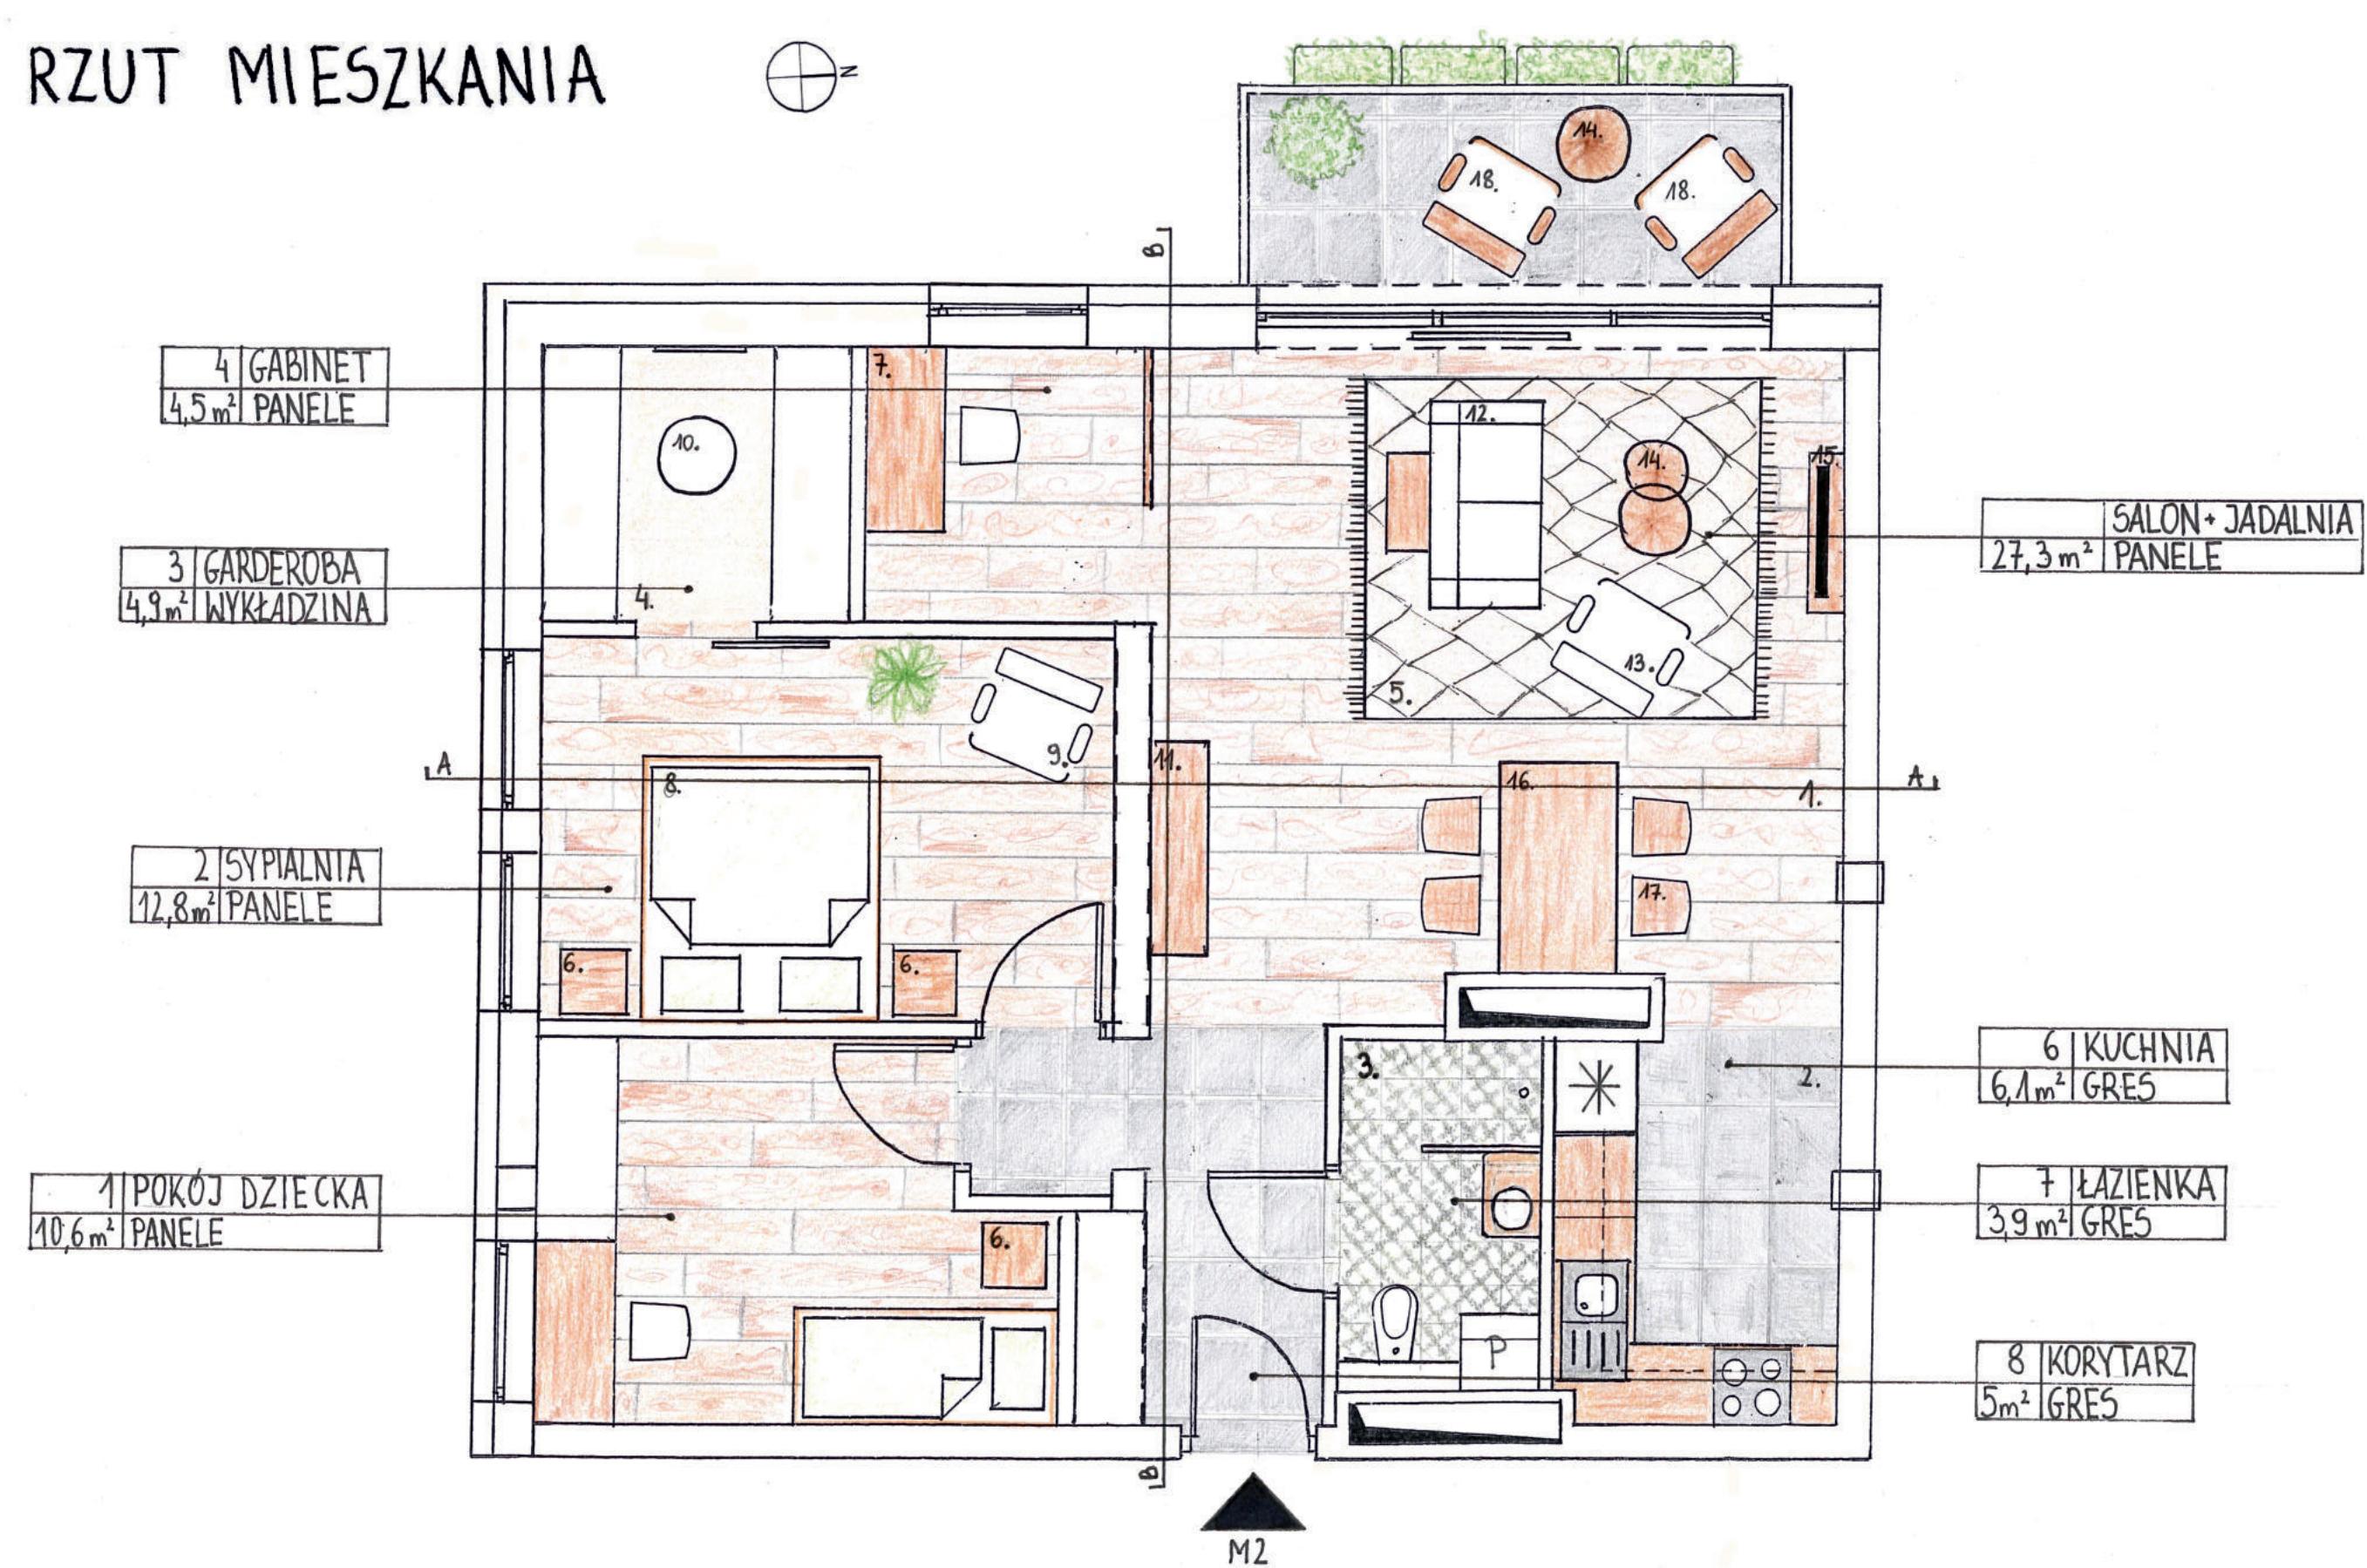

ZESTAWIENIE POWIERZCHNI UŻYTKOWEJ


POKÓJ DZIECKA 10.6 m²
SYPIALNIA 12.8 m²
GARDEROBA 4.9 m²
GABINET 4.5 m²
SALON + JADALNIA 27.3 m²
KUCHNIA 6.1 m²
ŁAZIENKA 3.9 m²

POWIERZCHNIA CAŁEGO MIESZKANIA 79,5 m²


CIĘŻ KOMUNIKACYJNY 5 m²

BALKON 6,4 m²

PERSPEKTYWA STREFY DZIENNEJ

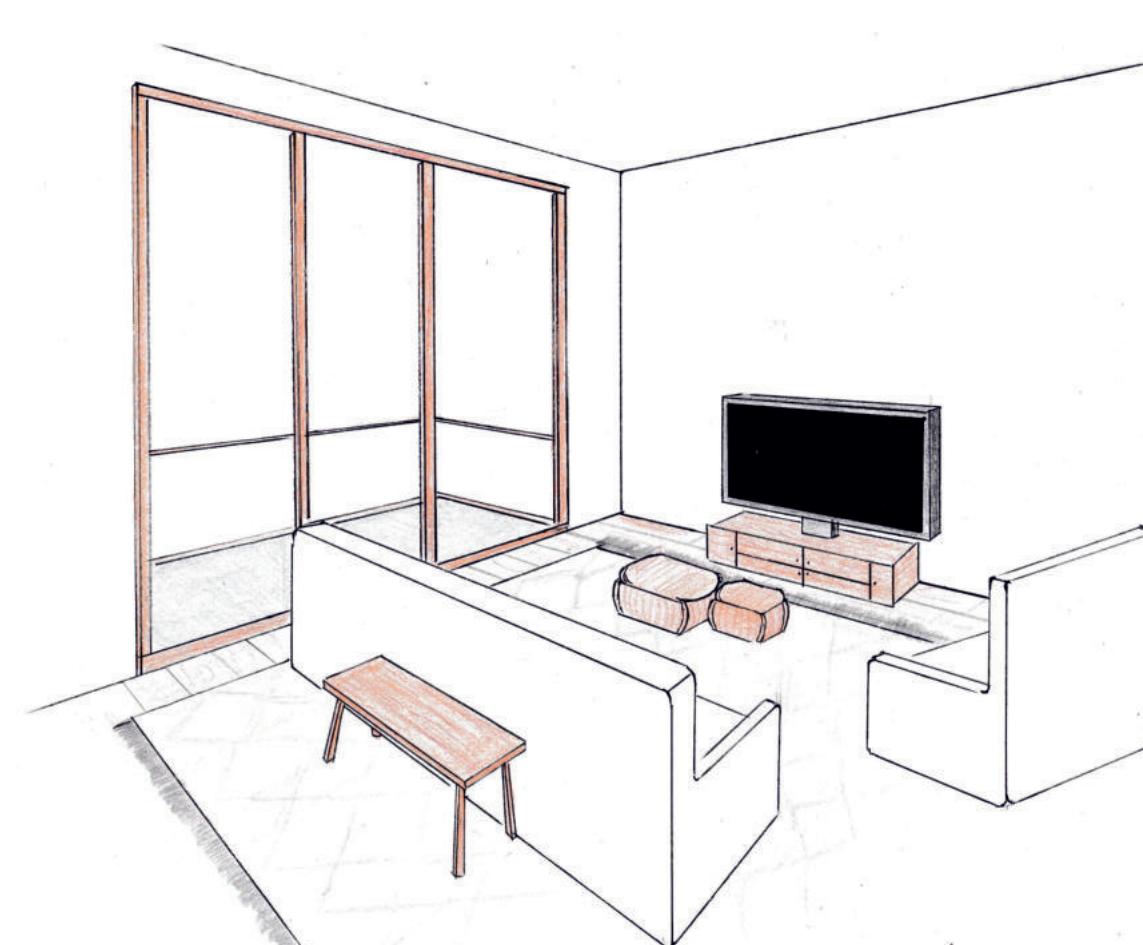

AKSONOMETRIA

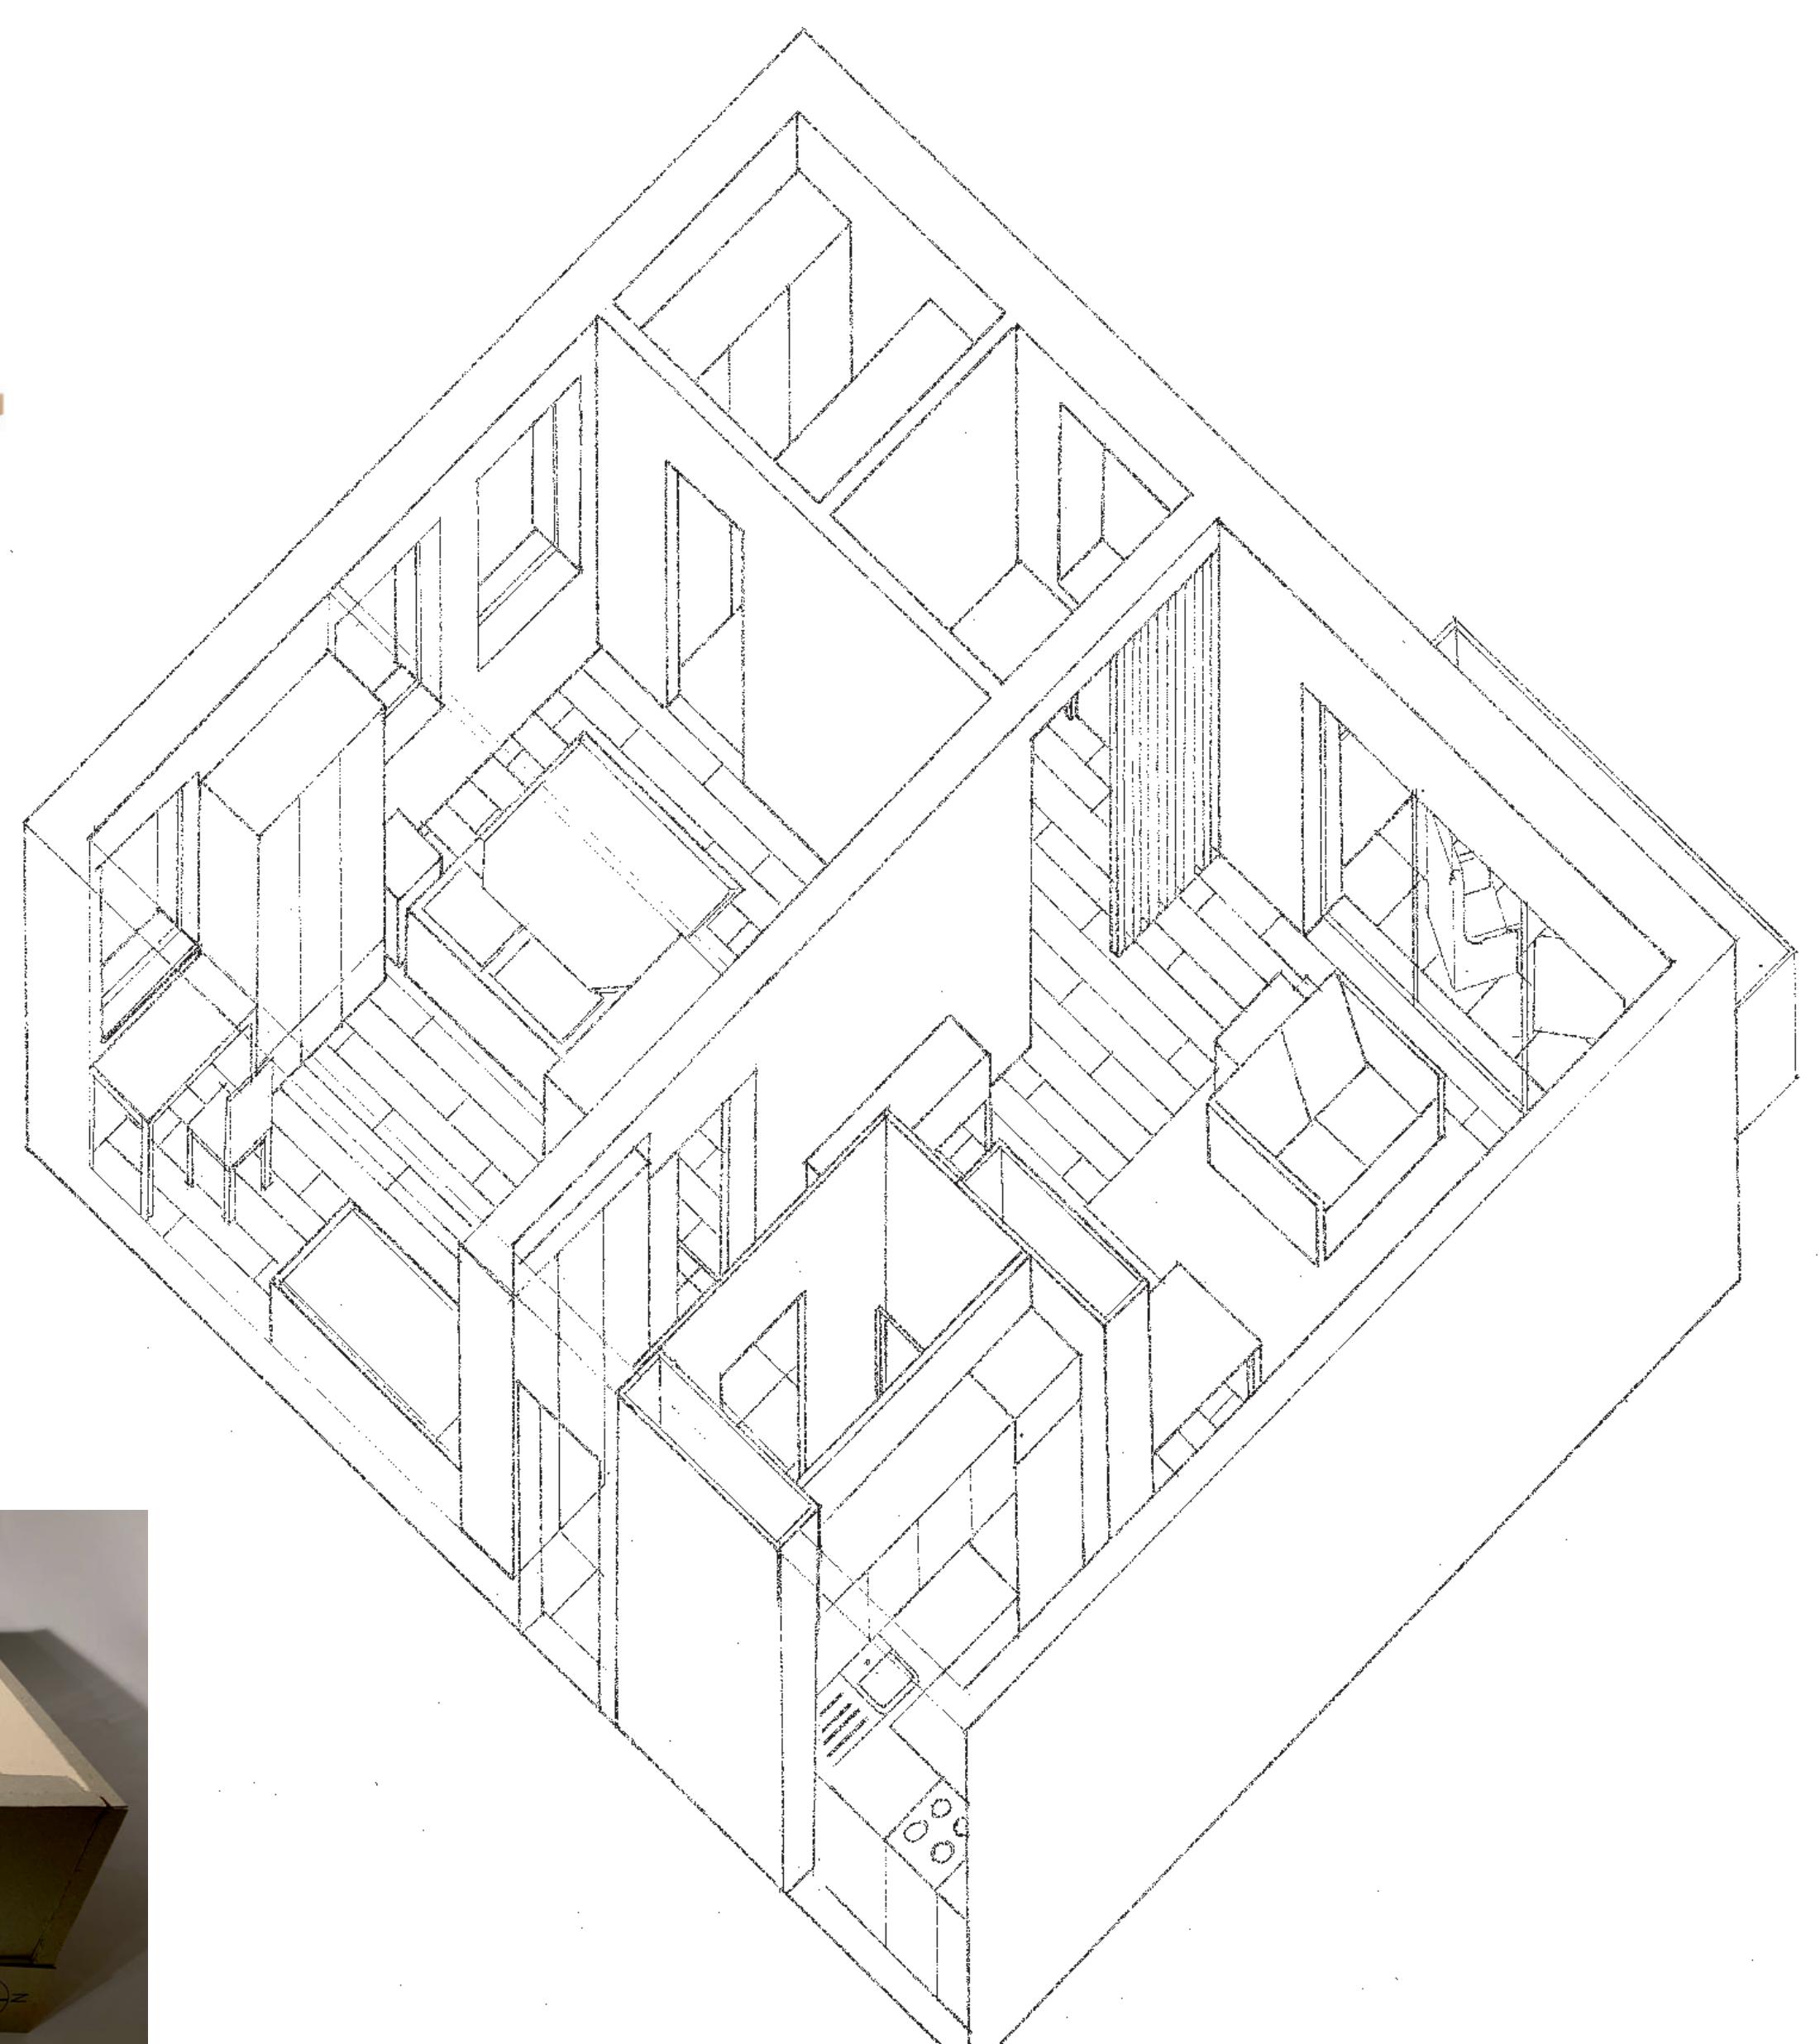


PRZEKRÓJ A-A




- 1. DRZWI PRZEGUWCHE, RENO
- 2. ŁÓŻKO, ODYS
- 3. FOTEL, VICKY
- 4. KONSOLA, ROMEO
- 5. KANAPA, VILDA
- 6. STÓŁ, AGO
- 7. FOTEL, LOBBY
- 8. SZAFKA RTV, FRANKLIN

PRZEKRÓJ B-B

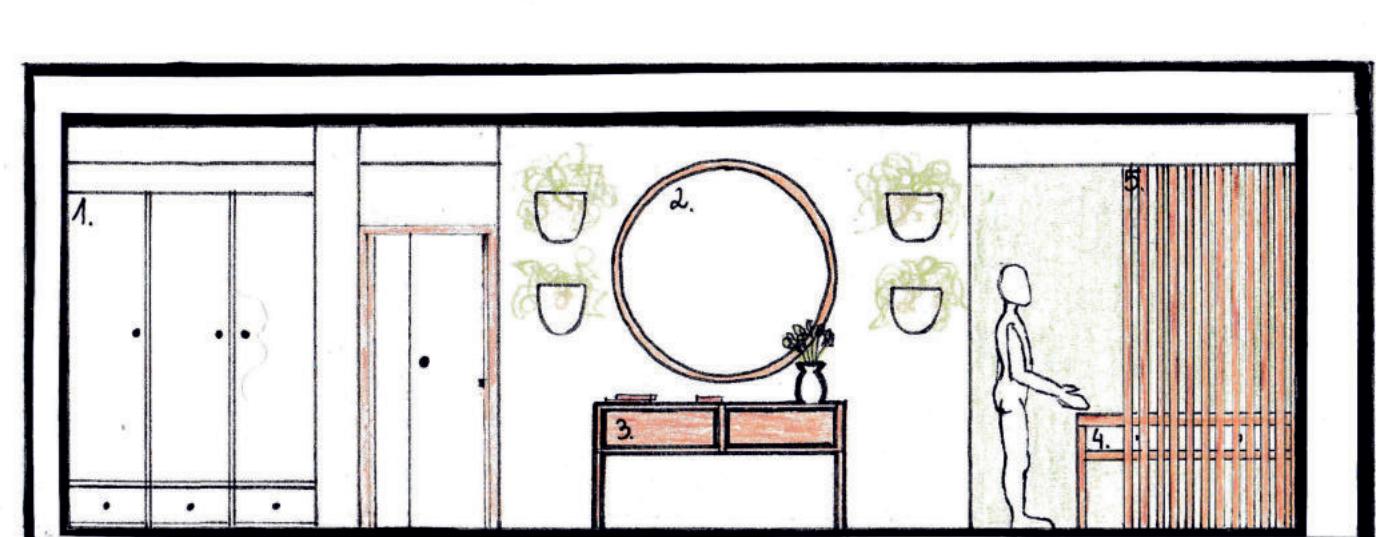


- 1. SZAFKA NORDBY
- 2. LUSTRO, STOCKHOLM
- 3. KONSOLA, ROMEO
- 4. BIURKO, DECASTO
- 5. ŚCIANKA AZURONA

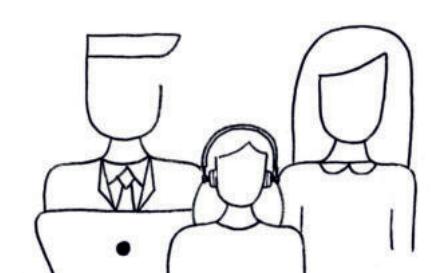

PROJEKT MIESZKANIA

RZUT ŁAZIENKI

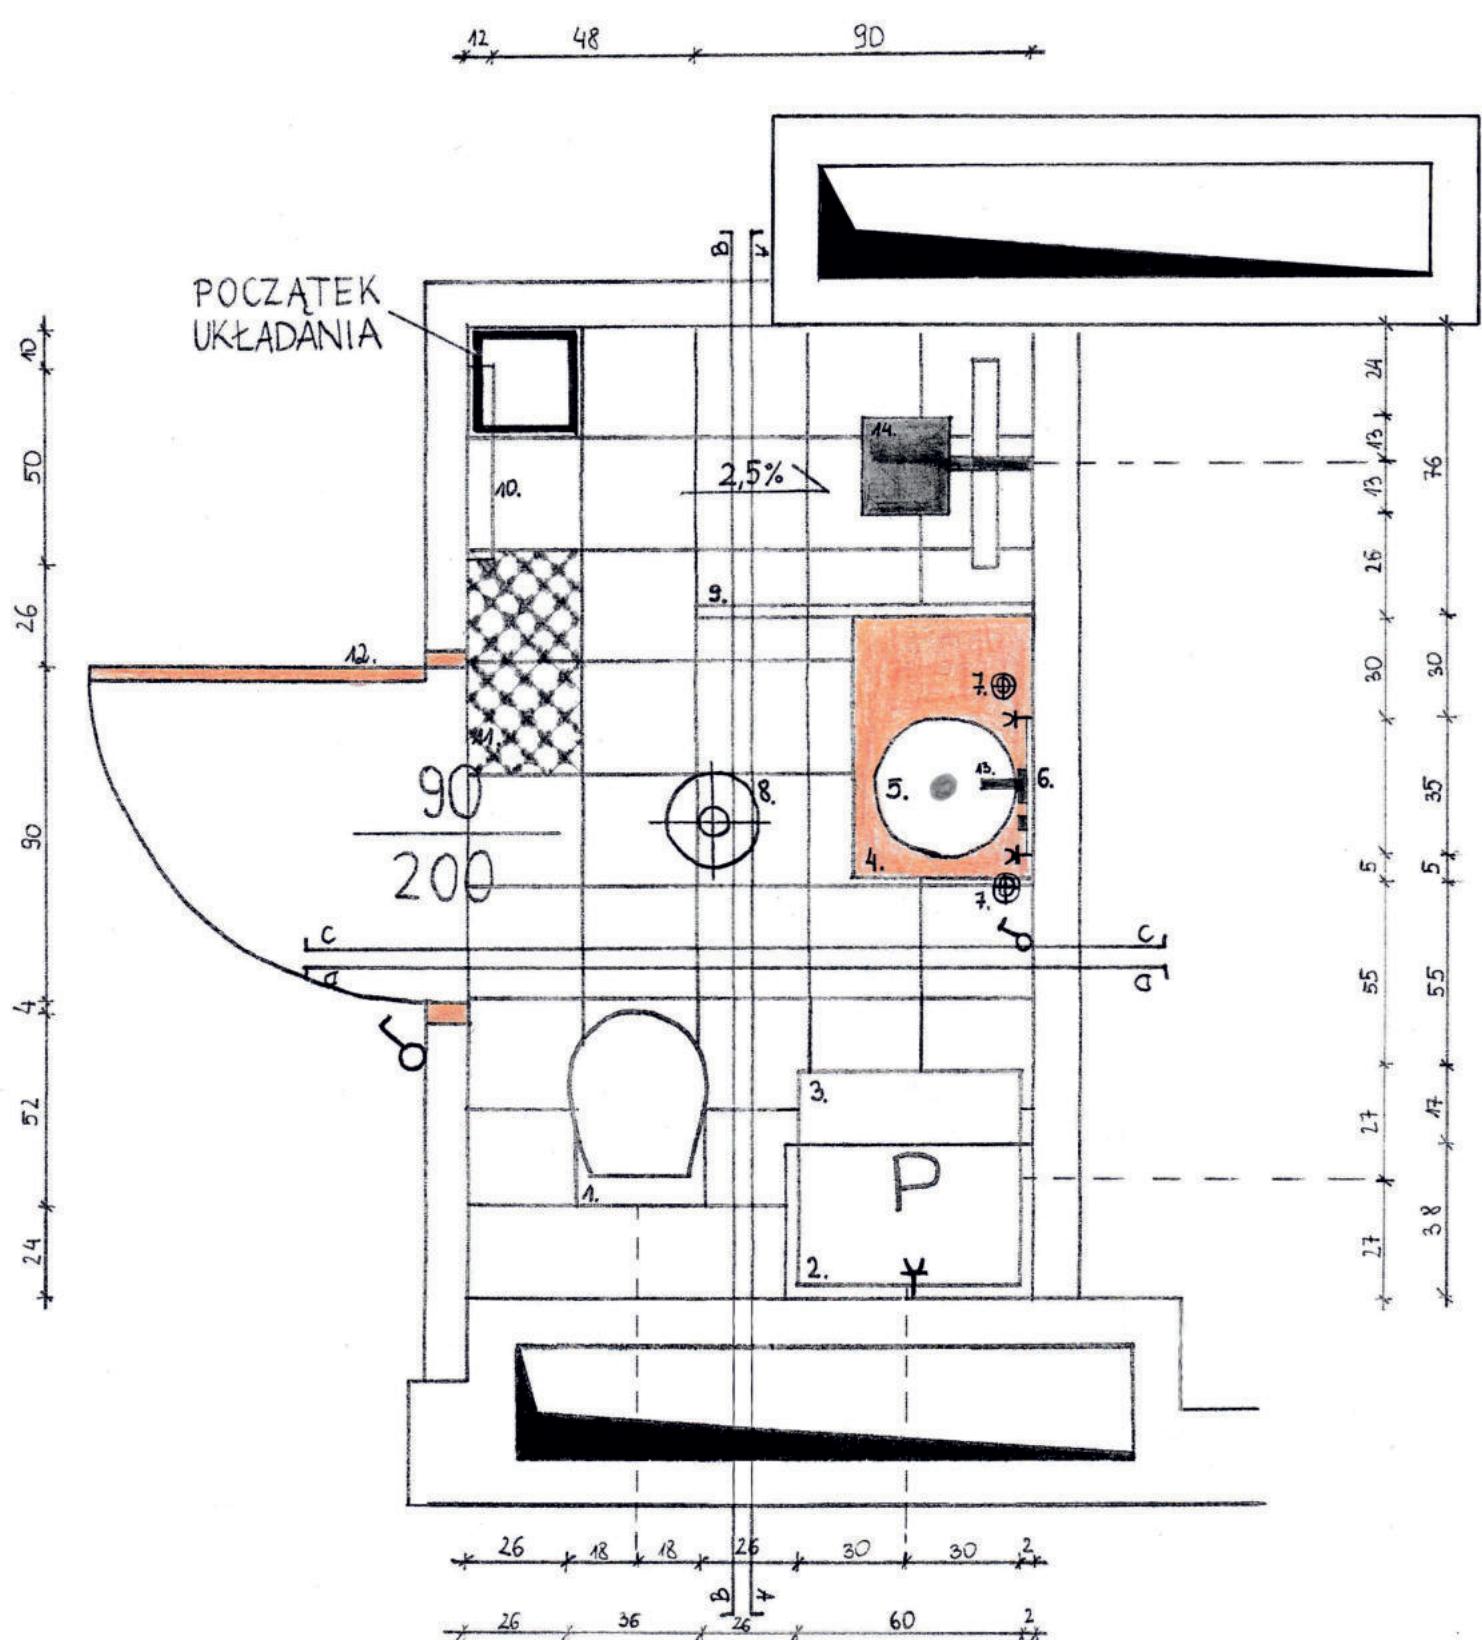

- 1. ŁĄCZNIK JEDNOBIEGOWY
- 2. Gniazdo wtyczkowe
- 3. Oprawa oświetleniowa natynkowa
- 4. Oprawa oświetleniowa wisząca
- 5. Miska WC, JOG OLTENS, 52x56x35 cm
- 6. Szafka nad pralke, STOŁARZ
- 7. Pralka WW70T4020CE SAMSUNG 55x60x85 cm
- 8. Szafka ŁAZIENKOWA, 2 BLATEM MEBLICO, 60x10x45 cm
- 9. Umywalka MODUO CERAMANT, 35x35x15 cm
- 10. Lustro SCANDI SLIM GERA DESIGN, 60x60 cm
- 11. Lampa SILICONE NOVODVORSKI, Ø 90 cm
- 12. Lampa SUFITOWA TOSA PLAFON, 20x20x10 cm
- 13. Ścianka PRYSZNICOWA, LOFT 73 SAN SNISS, 90x200 cm
- 14. Grzejnik ŁAZIENKOWY METEOR EXCELLENT, 50x85 cm
- 15. GRES SZKŁIANY PATCHWORK CONCEPT OPOCZNO, 30x30 cm
- 16. Drzwi RADEX LEROY MERLIN 90x200 cm
- 17. Bateria UMYWALKOWA MOLLE OLTENS,
- 18. ZESTAW PRYSZNICOWY, CROMETTA HANSGROHE 24cm x 24 cm

KŁAD A-A





KŁAD B-B

PERSPEKTYWA ŁAZIENKI




KŁAD C-C

KŁAD D-D

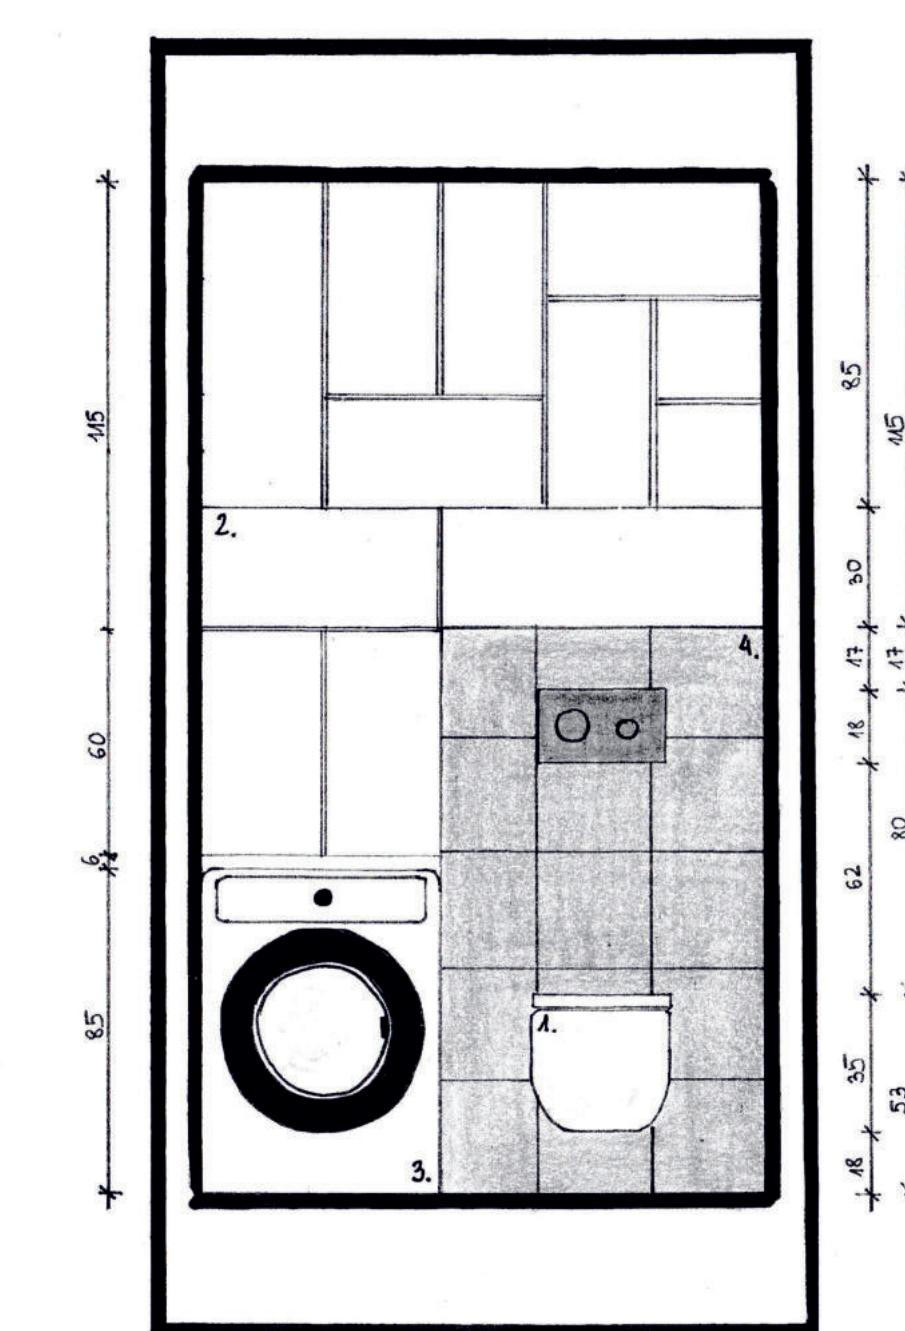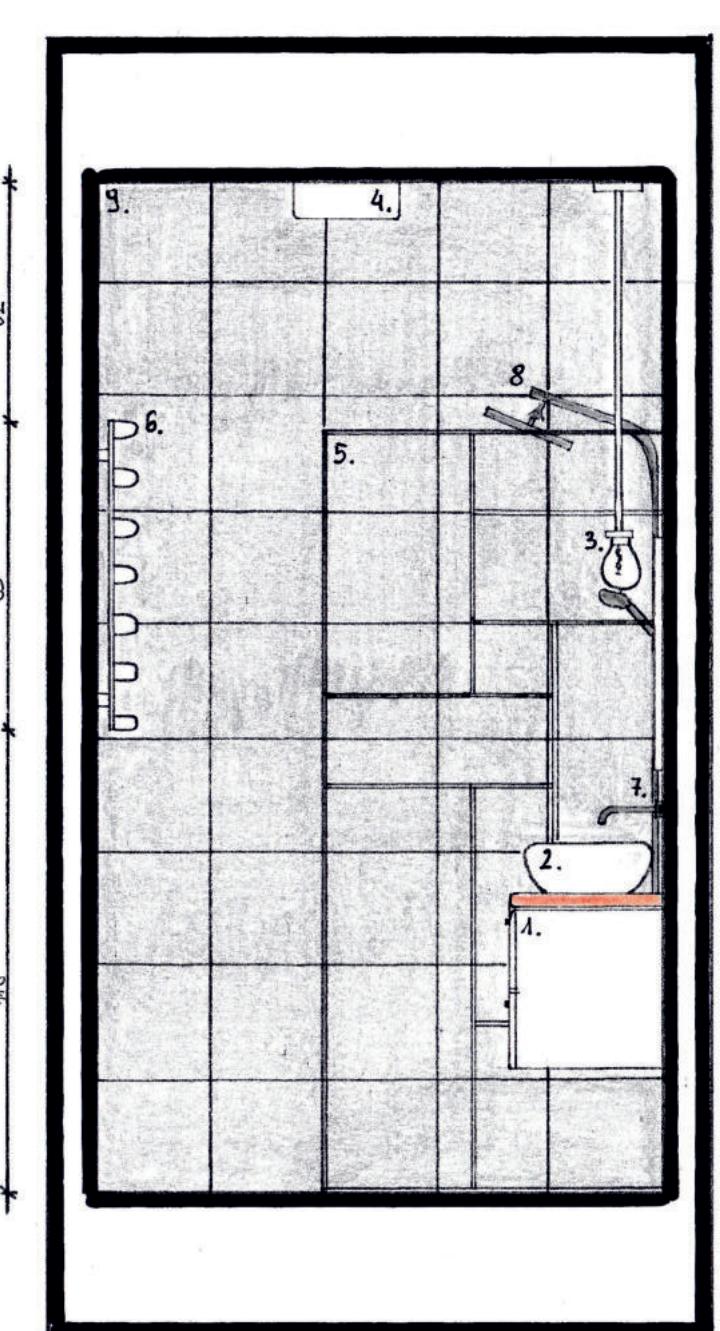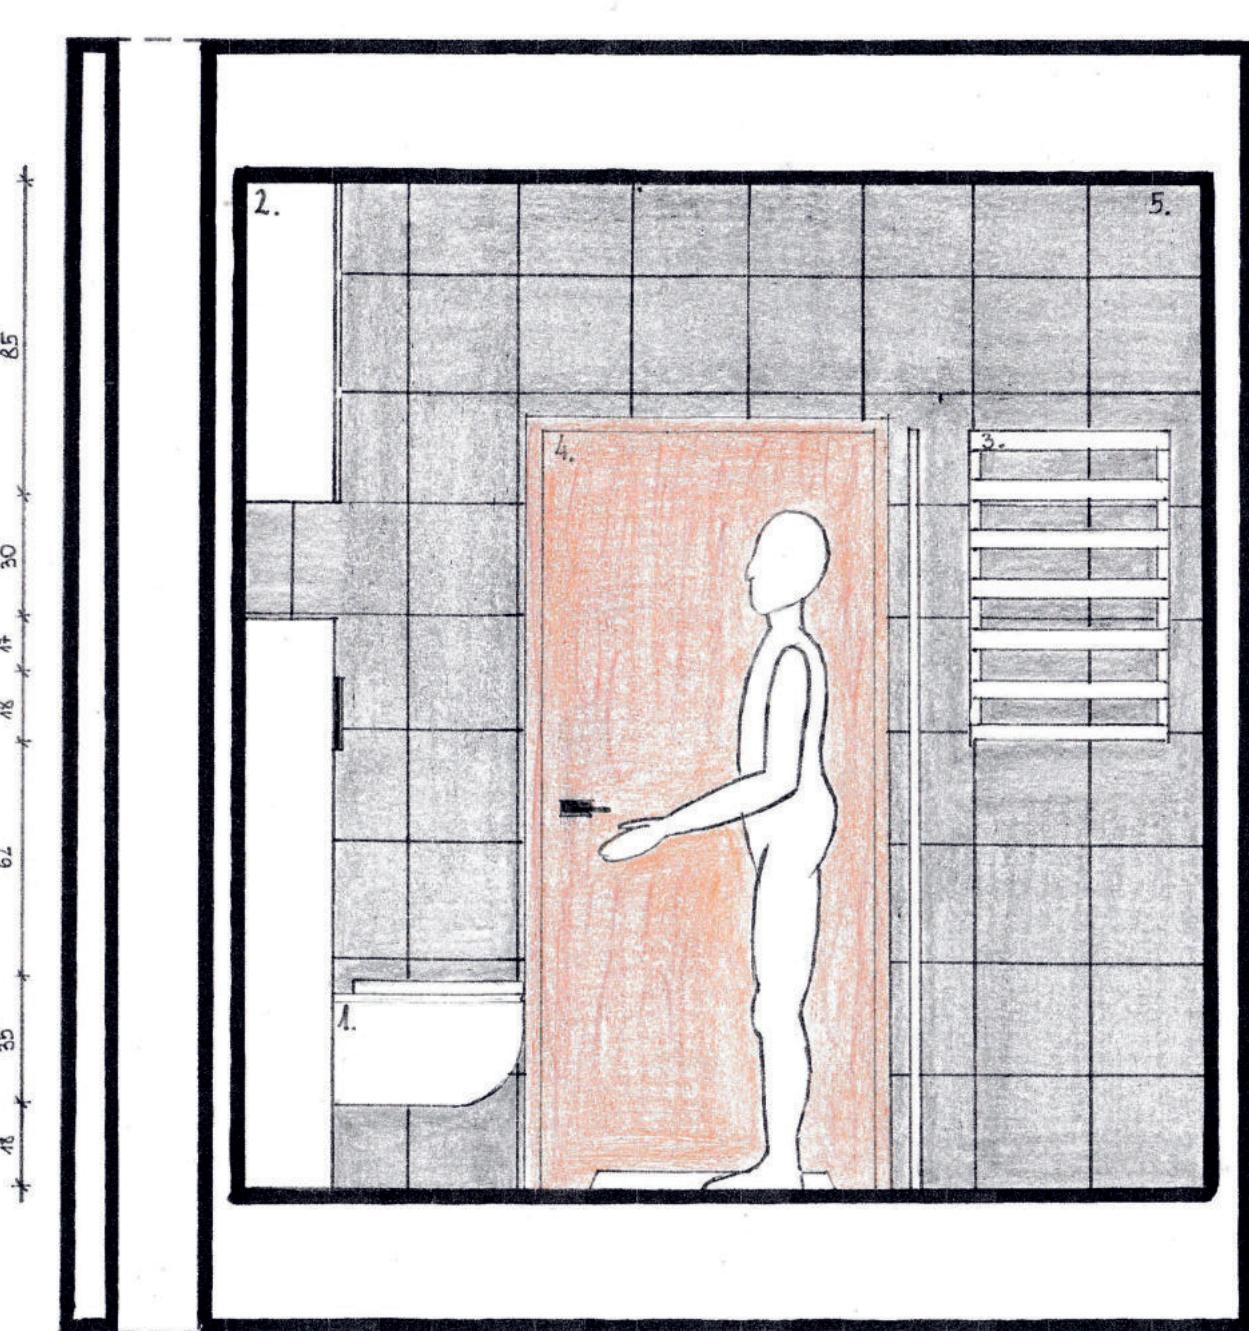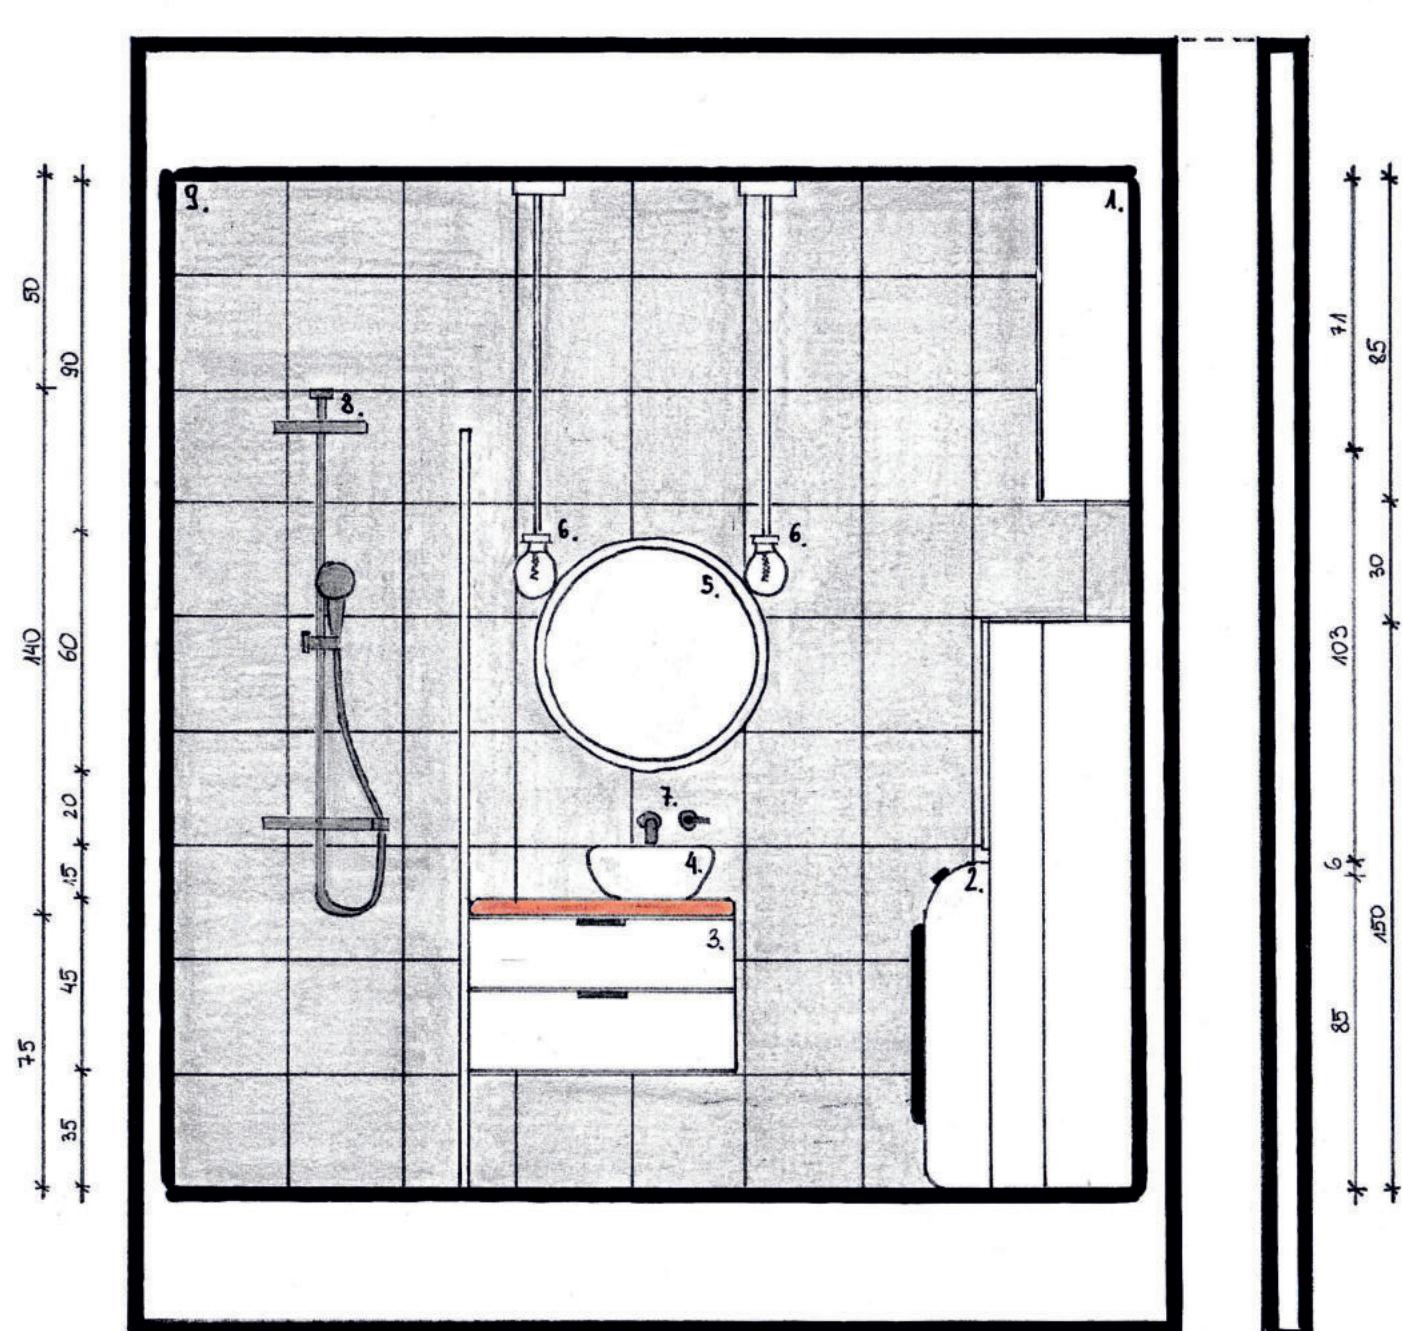

RZUT KUCHNI


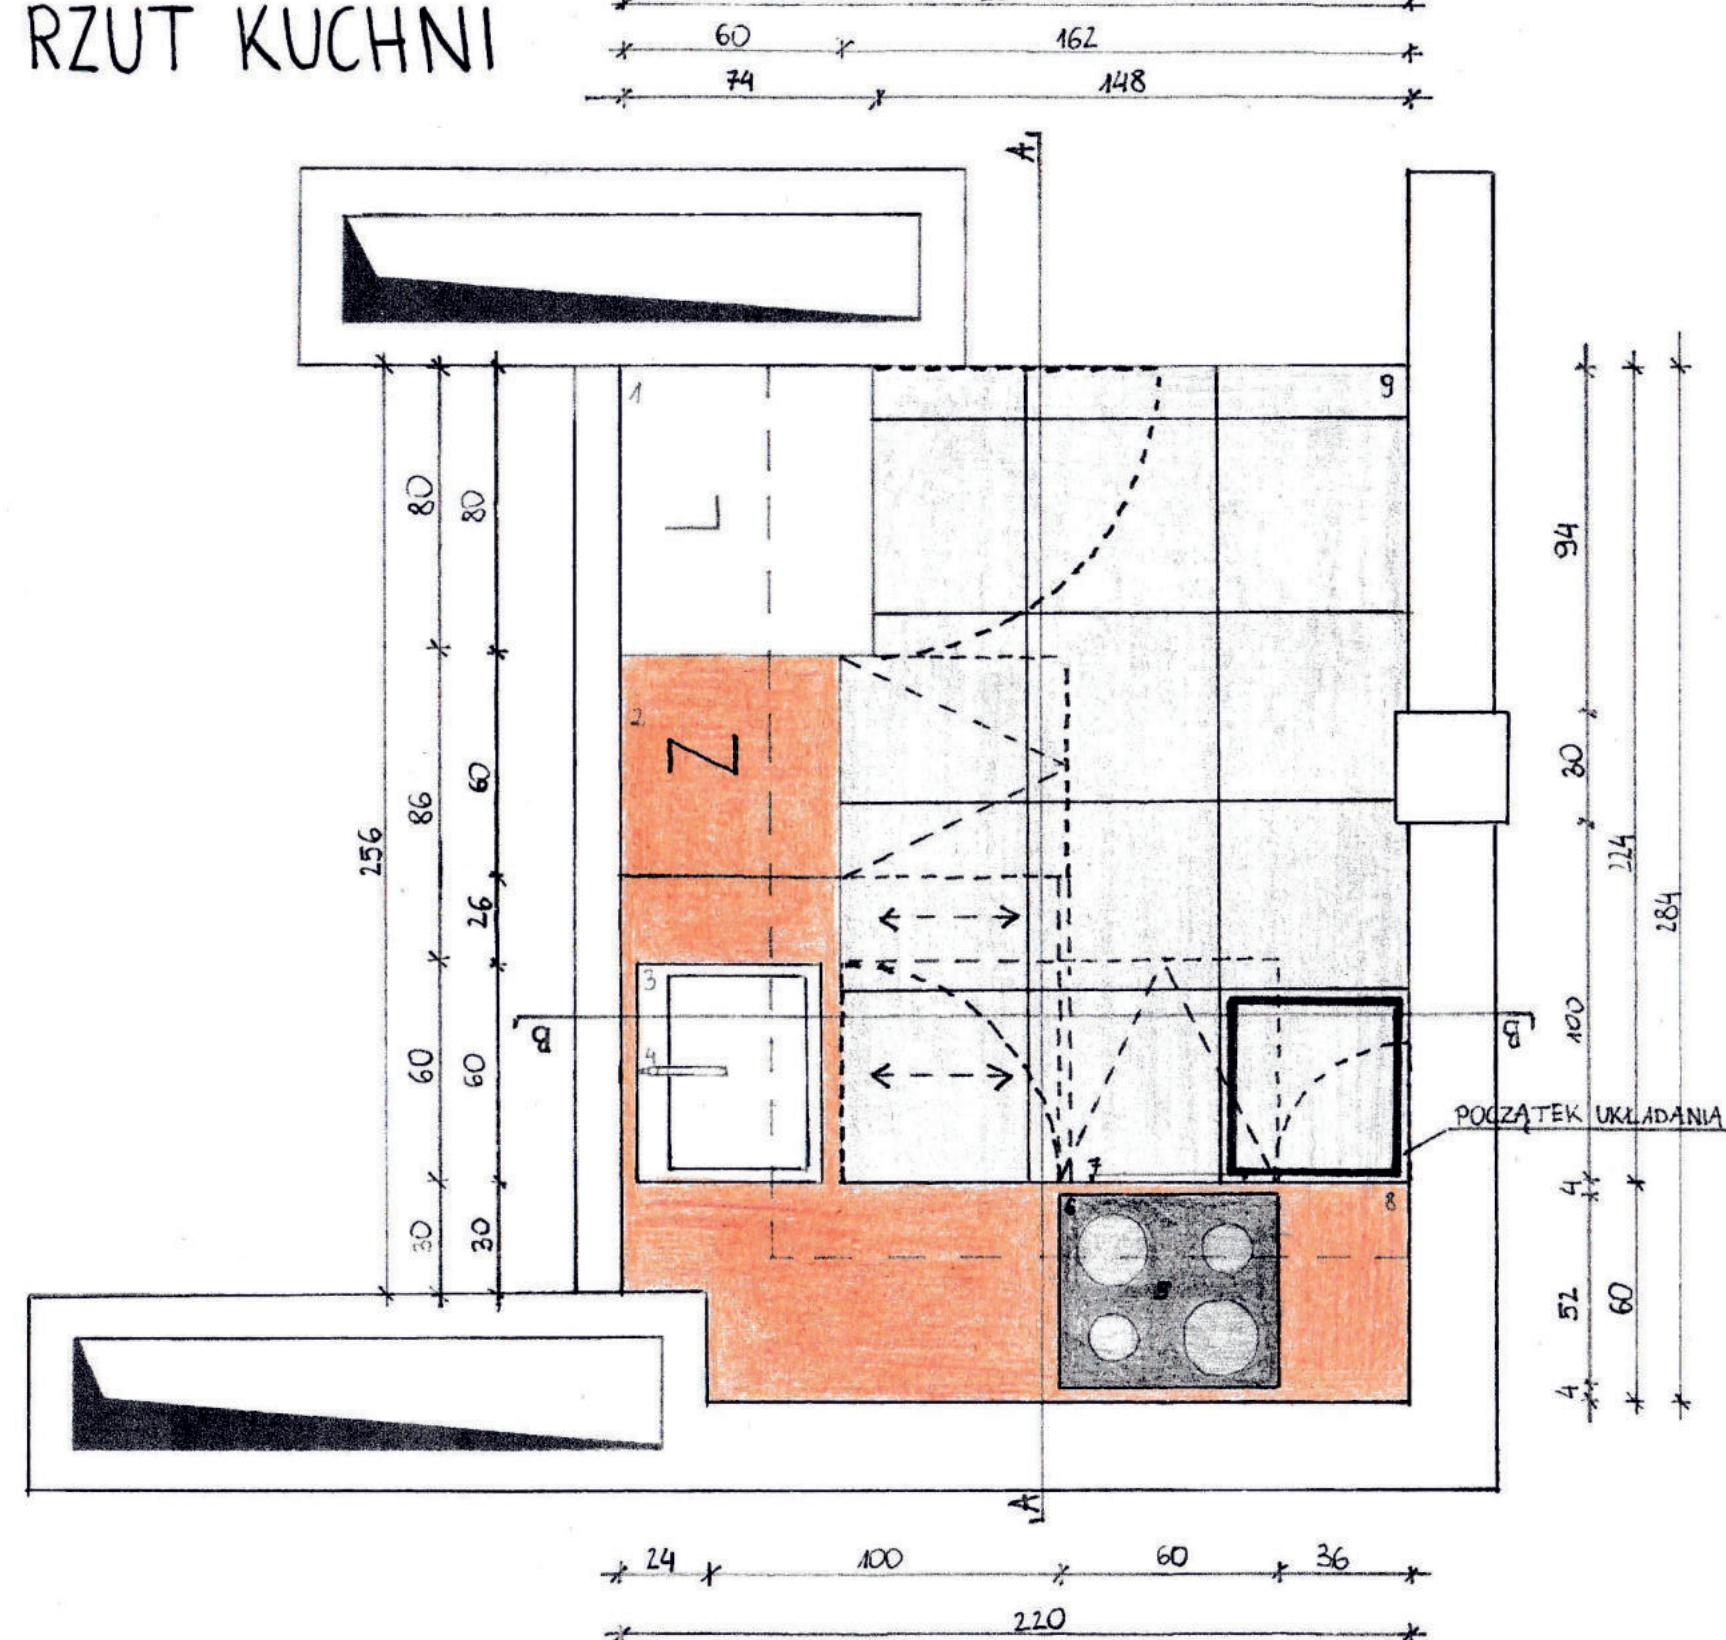


- 1. ŁĄCZNIK ŚWIĘCZNIKOWY
- 2. Gniazdo wtyczkowe
- 3. Oprawa oświetleniowa wbudowana
- 4. Lodówka SMEG, 48x5x80,4x73,5 cm
- 5. Zmywarka BOSCH, 60x81,5x55 cm
- 6. Zlewozmywak, ZANTE GRANITAN, 619x512 mm
- 7. Bateria KUCHENNA, AGLO GRANITAN, NYS 300 mm
- 8. Okap AMICA, 55x4,6x29 cm
- 9. Płyta indukcyjna BOSCH, 59,2x52,2 cm
- 10. Piekarnik ELECTROLUX, 60x60x56 cm
- 11. Blat i szafki STOŁARZ
- 12. Płytki ANTARES IMOLA, 50x50 cm

PERSPEKTYWA KUCHNI



KŁAD A-A

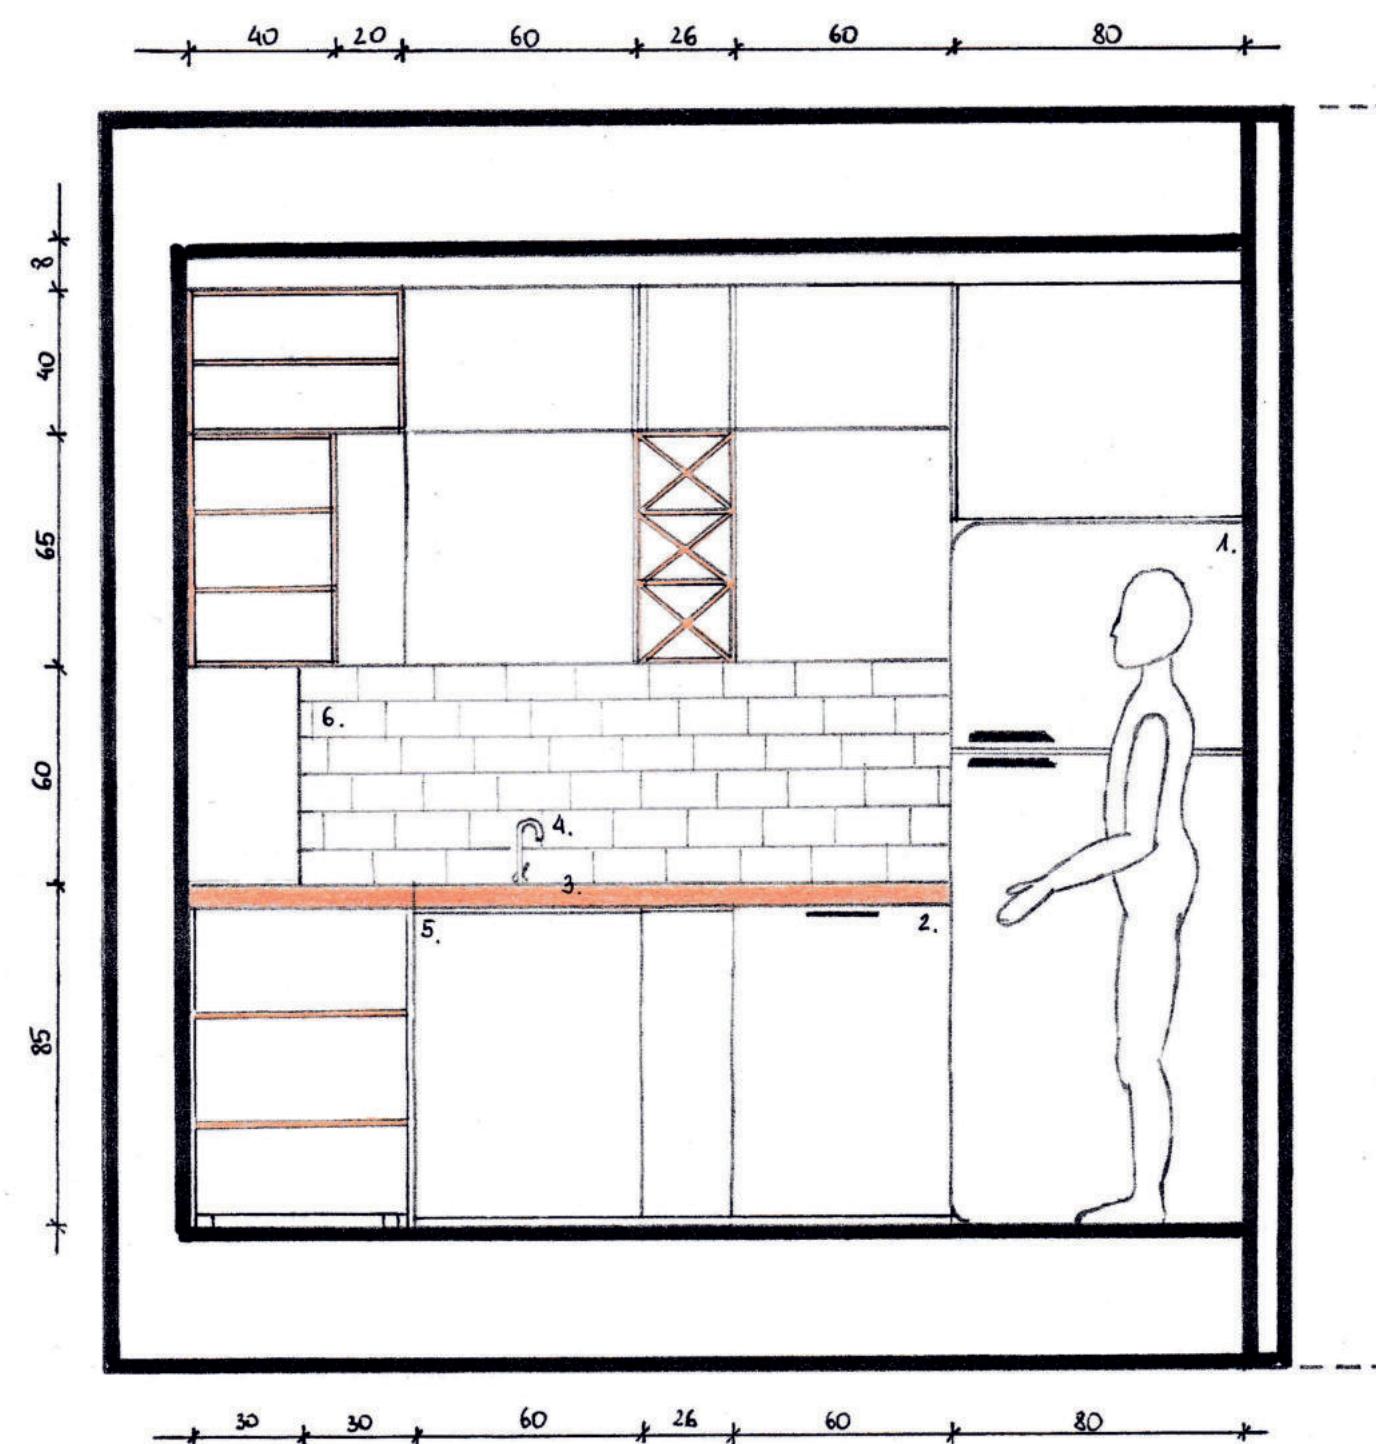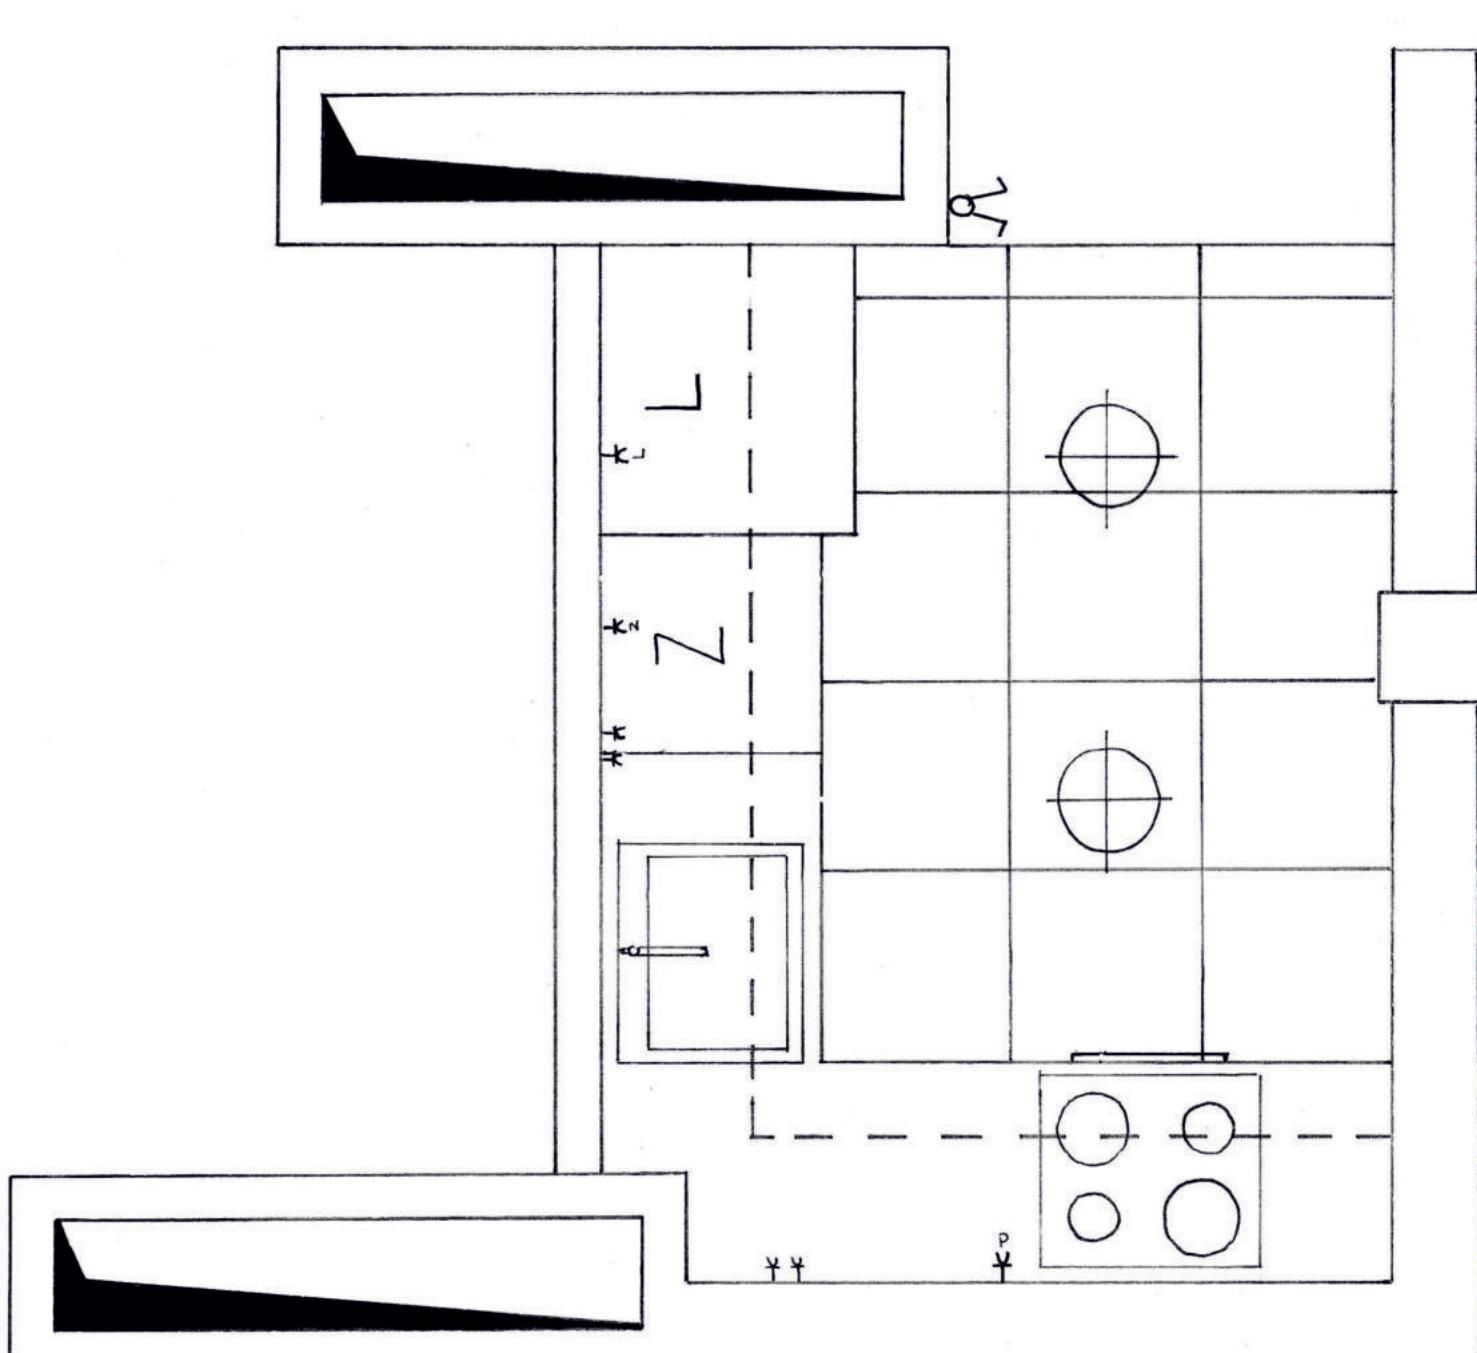

KŁAD B-B

